
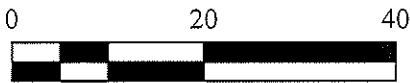


NOTICE
BEFORE DESIGN BEGINS ON THE SUBJECT PROPERTY
THE OWNER SHOULD CHECK THE LOCAL GOVERNING
AUTHORITIES ABOUT BUILDING SETBACKS AND OTHER
BUILDING REQUIREMENTS.


BEARING BASIS:
BEARINGS ARE GRID NORTH BASED ON THE TEXAS
COORDINATE SYSTEM CENTRAL TEXAS ZONE (4203)
NAD83 HARN HORIZONTAL CONTROL.

TREE LIST	
23	21.5" SPANISH OAK (P) (M)
38	21.5" LIVE OAK (P)
39	19.25" LIVE OAK (P)
41	15.5" LIVE OAK
70	13.5" SPANISH OAK

LEGEND	
	1/2" ROD FOUND
	1/2" ROD W/CAP SET "ALLSTAR 5729"
	MAG NAIL SET
	WIRE FENCE
	CHAIN LINK FENCE
	WOOD FENCE
	RECORD INFORMATION
	WATER METER
	UTILITY POLE
	ELECTRIC METER
	OFF
	TREE
	MULTI-STEMMED TREE
	PROTECTED TREE (OVER 19")
	P.O.B. POINT OF BEGINNING

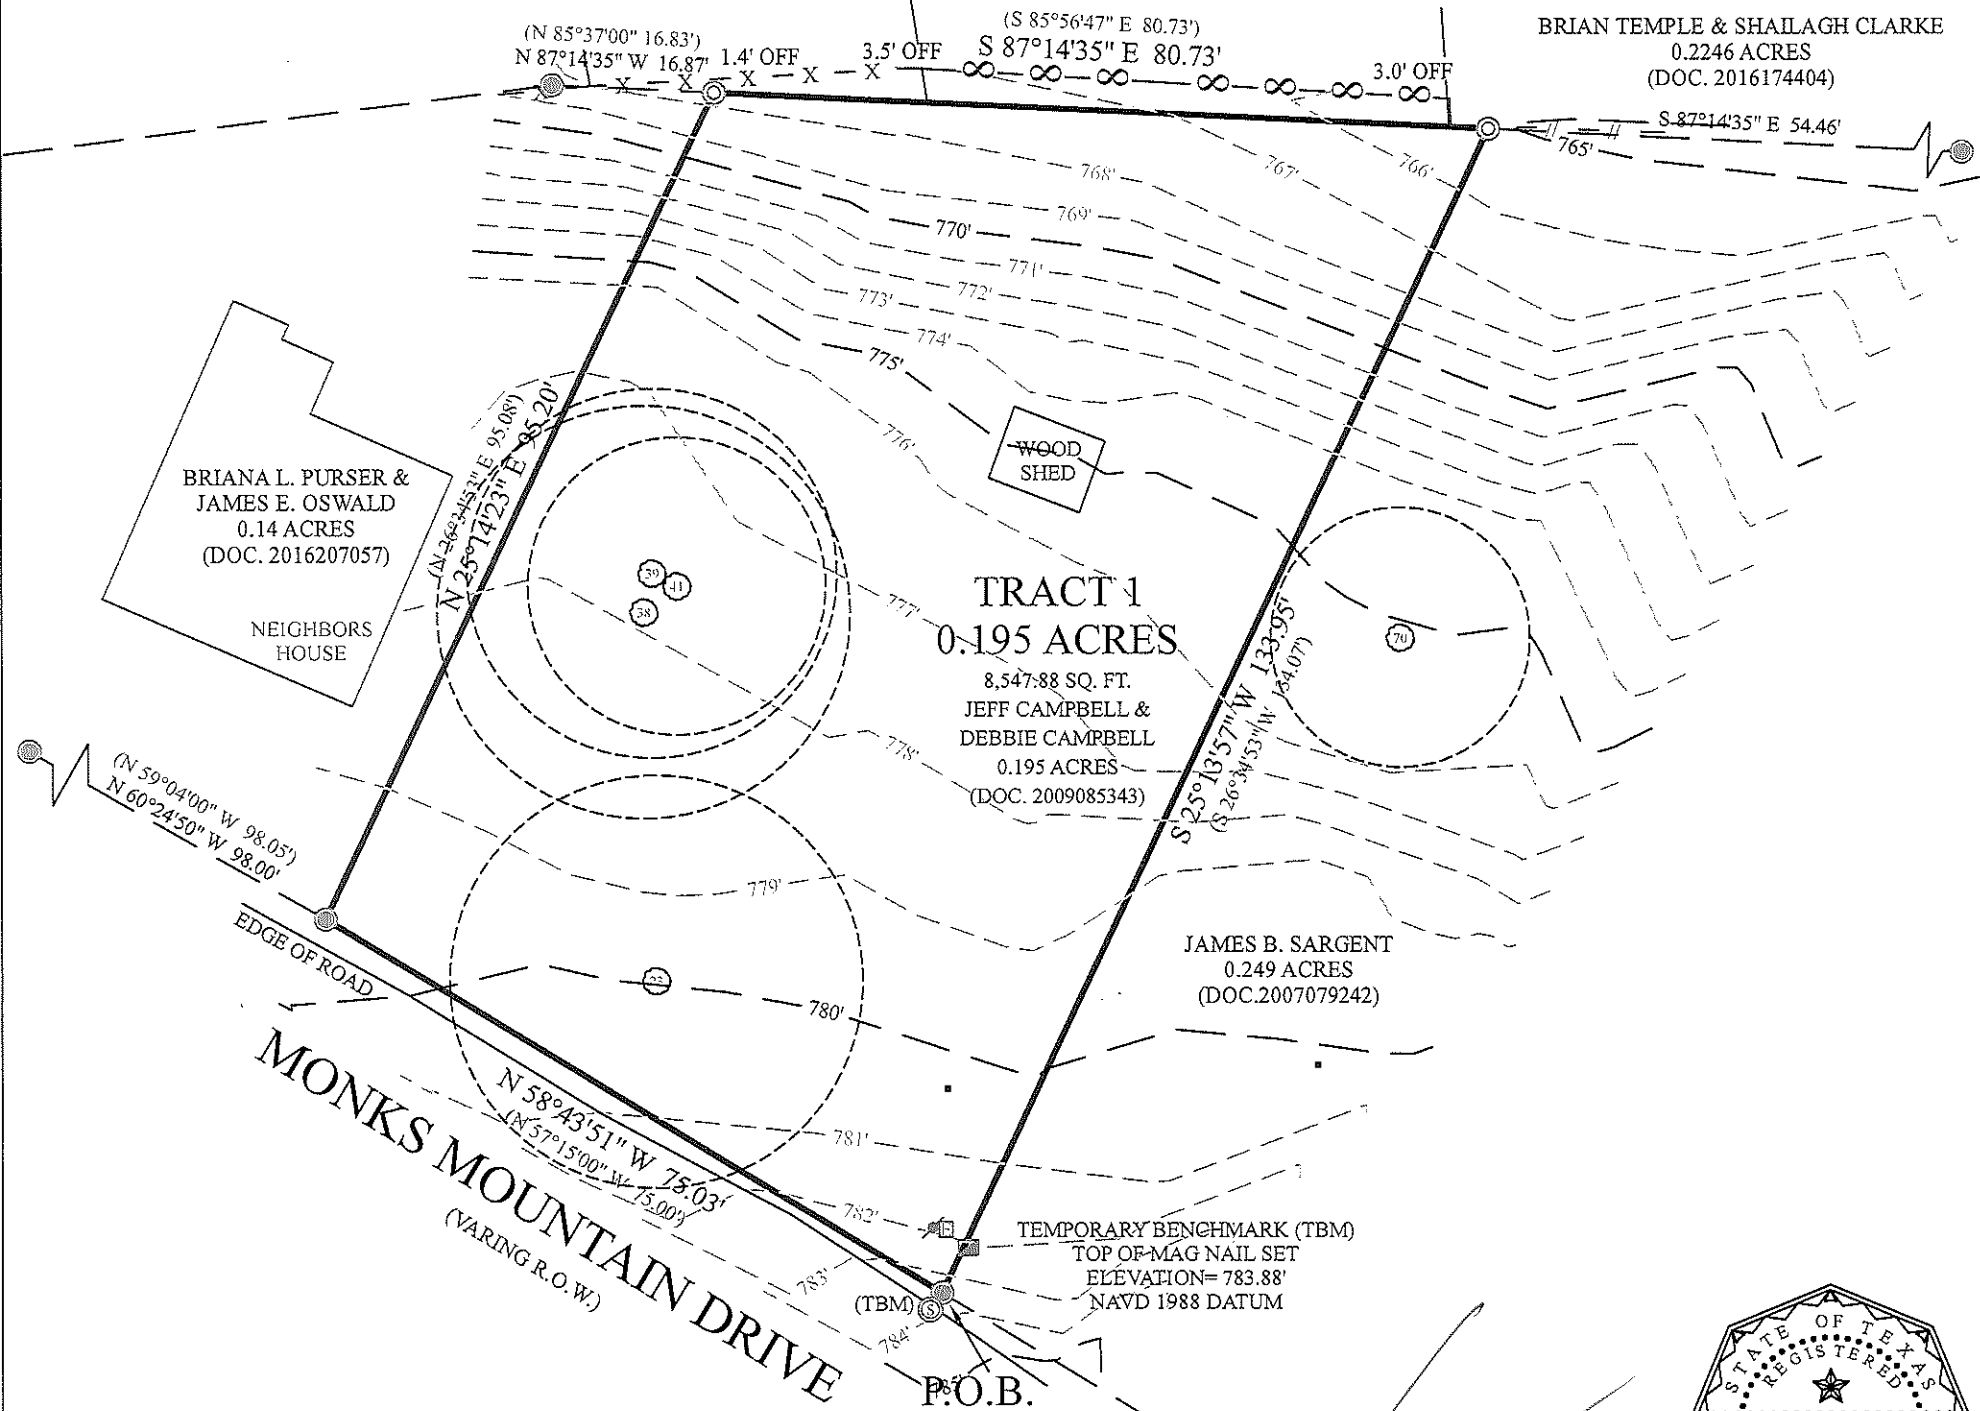

TO THE LIEN HOLDER AND / OR OWNERS OF THE PREMISES SURVEYED
I DO HEREBY CERTIFY THAT THIS SURVEY SUBSTANTIALLY COMPLIES
WITH THE CURRENT TEXAS SOCIETY OF PROFESSIONAL SURVEYORS
MANUAL OF PRACTICE REQUIREMENTS FOR A CATEGORY 1 CONDITION
SURVEY. THIS SURVEY WAS PERFORMED WITHOUT THE
BENEFIT OF AN ABSTRACT OF TITLE. NO EASEMENT RESEARCH HAS BEEN
PERFORMED.

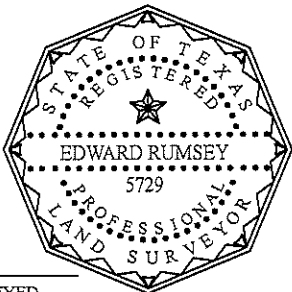


RESTRICTIONS

RESTRICTIONS:
THIS SURVEY WAS PREPARED WITHOUT THE BENEFIT OF A TITLE COMMITMENT AND THIS SURVEYOR DID NOT RESEARCH THE DEED RECORDS FOR PREVIOUS CONFLICTS IN
TITLE, EASEMENTS AND/OR BOUNDARY LINE AGREEMENTS, THEREFORE, CERTAIN EASEMENTS MAY HAVE BEEN GRANTED WHICH ARE NOT REFLECTED HEREON. ONLY THOSE
SETBACK LINES, EASEMENTS, BOUNDARY LINES AND INTERESTS WHICH ARE REPRESENTED ON THE PARENT SUBDIVISION PLAT, WHICH IS REFERENCED HEREON, ARE PLOTTED
ON THIS SURVEY, NO DOCUMENTS OTHER THAN THOSE CITED ON THIS SURVEY HAVE BEEN EXAMINED.

LEGAL DESCRIPTION

BEING 0.195 OF AN ACRE OF LAND OUT OF B.K. STEWART SURVEY NUMBER 84, ABSTRACT NUMBER 2453, TRAVIS COUNTY, TEXAS, SAME BEING THAT CERTAIN JEFF
CAMPBELL AND DEBBIE CAMPBELL 0.195 ACRE TRACT RECORDED IN DOCUMENT NUMBER 2009085343, OFFICIAL PUBLIC RECORDS, TRAVIS COUNTY, TEXAS, SAID 0.195
OF AN ACRE OF LAND TO BE MORE PARTICULARLY DESCRIBED BY METES AND BOUNDS IN EXHIBIT "A", ATTACHED HERETO AND MADE A PART HEREOF.

F.I.R.M. MAP INFORMATION		ADDRESS			
THIS PROPERTY DOES NOT LIE WITHIN THE 100 YEAR FLOOD - PLAIN, AND HAS A ZONE "X" RATING AS SHOWN ON THE FLOOD INSURANCE RATE MAPS F.I.R.M. MAP NO. 48453C0215J PANEL: 0215J DATED: 01/22/2020 THIS CERTIFICATION IS FOR INSURANCE PURPOSES ONLY AND IS NOT A GUARANTEE THAT THIS PROPERTY WILL OR WILL NOT FLOOD. CONTACT YOUR LOCAL FLOOD PLAIN ADMINISTRATOR FOR THE CURRENT STATUS OF THIS TRACT.		JEFF CAMPBELL & DEBBIE CAMPBELL 16200 MONKS MOUNTAIN DRIVE AUSTIN, TRAVIS COUNTY, TEXAS			
		SURVEY DATE:	MARCH 02, 2021	FIELD BY:	JACOB BROWN
		TITLE CO.:	-	CALC. BY:	CHRIS ZOTTER
		G.F. NO.:	-	DRAWN BY:	DAVID BAK
		JOB NO.:	A0208421	UPDATE BY:	-
		RPLS CHECK:	EDWARD RUMSEY		03/02/2021

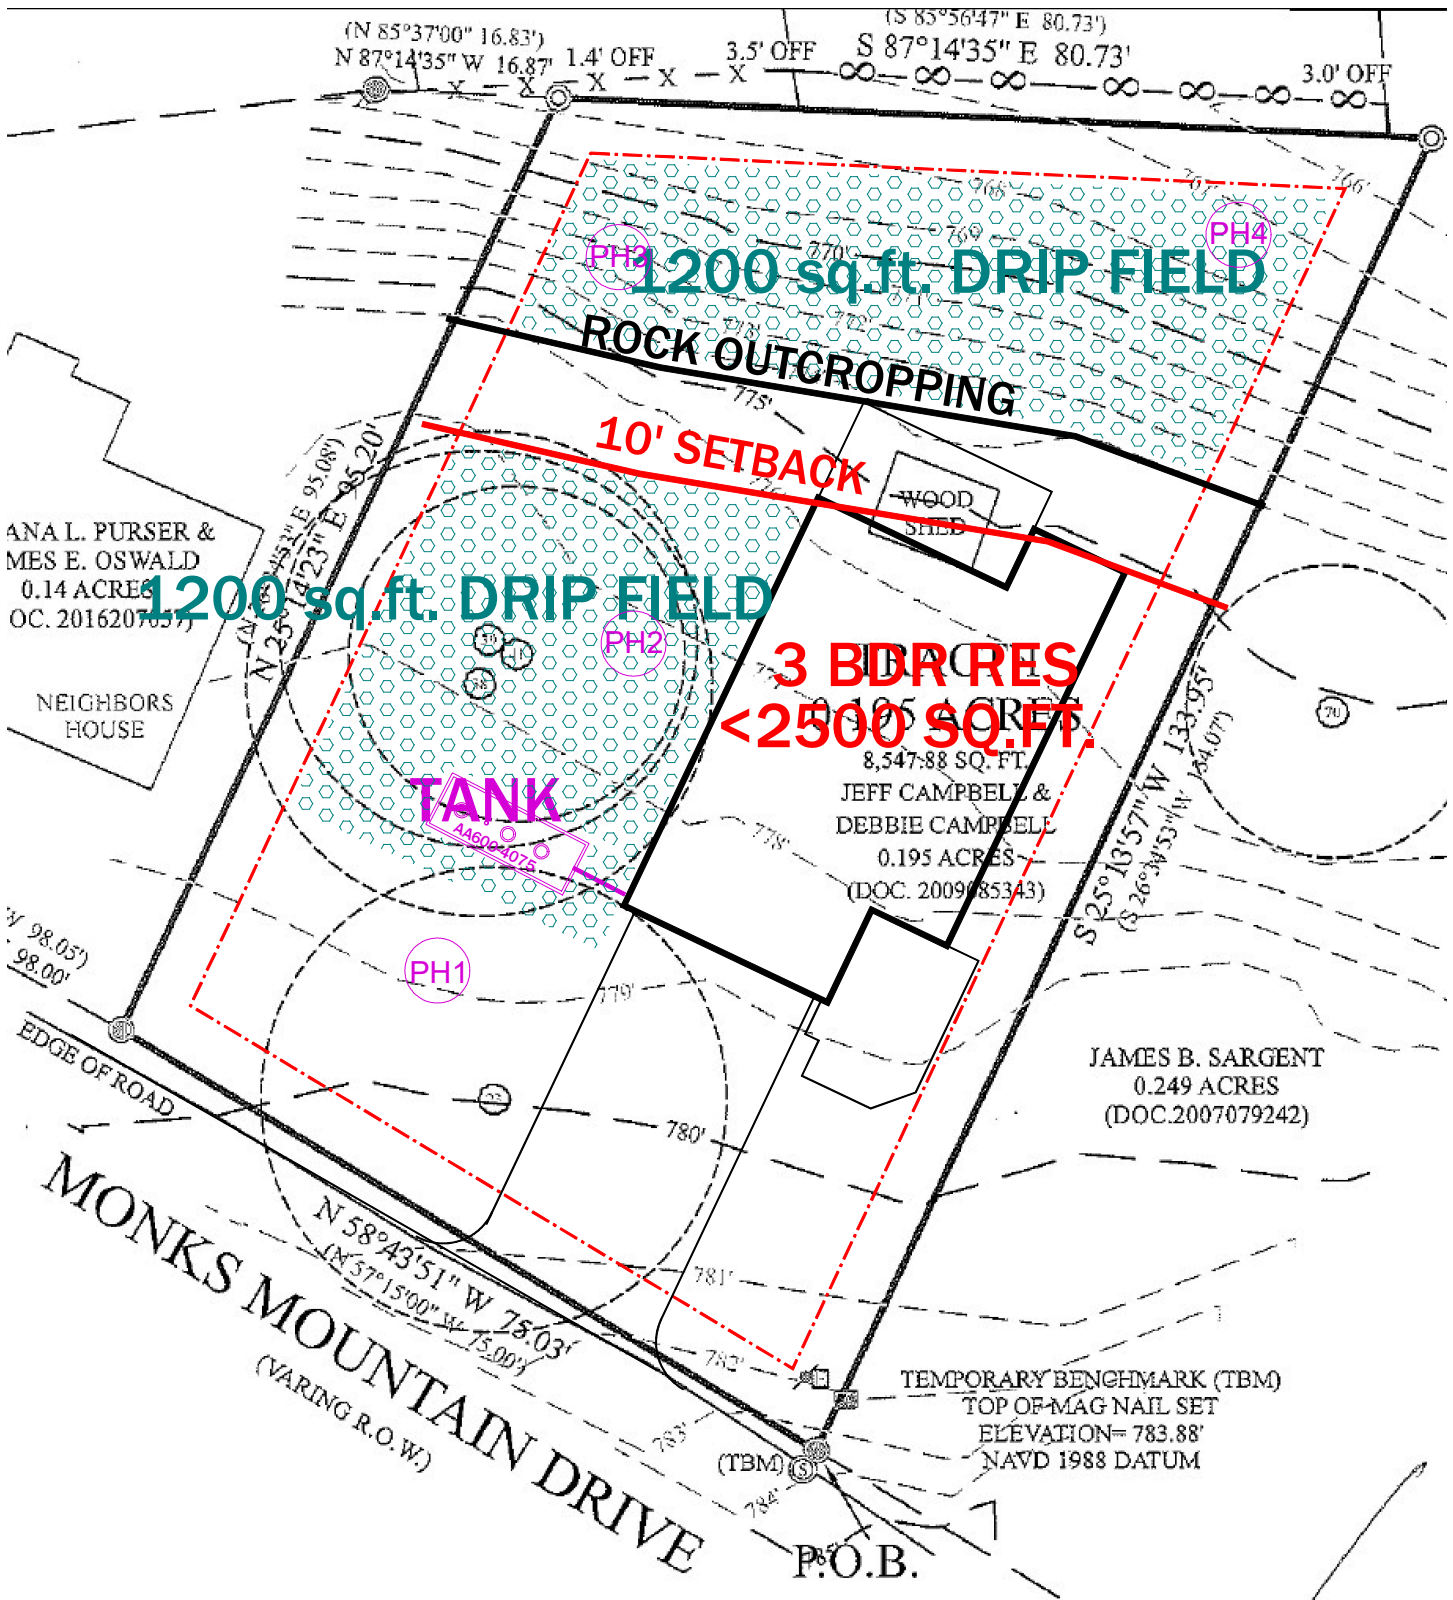

ANA L. PURSER &
MES E. OSWALD
0.14 ACRES
OC. 2016207057

NEIGHBORS
HOUSE

1200 sq.ft. DRIP FIELD

10' SETBACK

1200 sq.ft. DRIP FIELD

ROCK OUTCROPPING

3 BDR RES
<2500 SQ.FT.

TANK

JEFF CAMPBELL &
DEBBIE CAMPBELL
0.195 ACRES
(DOC. 2009785343)

JAMES B. SARGENT
0.249 ACRES
(DOC.2007079242)

MONKS MOUNTAIN DRIVE
(VARIING R.O.W.)

TEMPORARY BENCHMARK (TBM)
TOP OF MAG NAIL SET
ELEVATION = 783.88'
NAVD 1988 DATUM

P.O.B.