




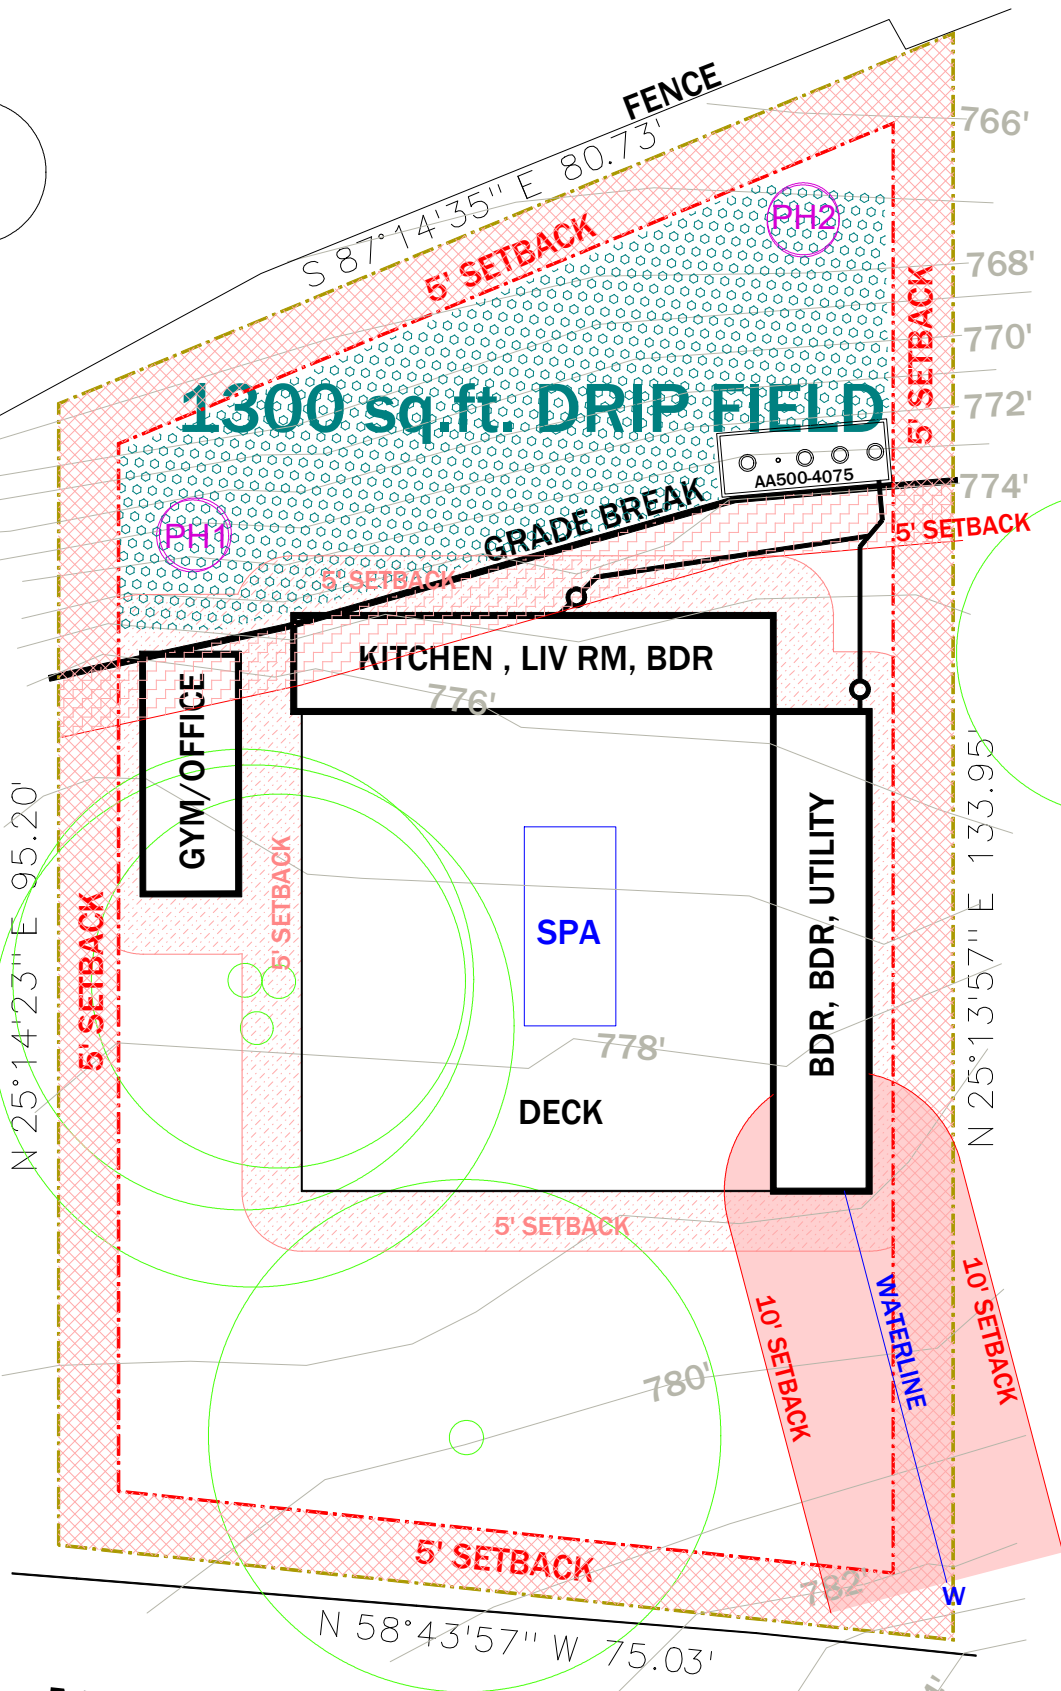

SETBACKS	
	WATER LINE
	PROPERTY/PUE
	SURFACE IMPROVEMENTS
	BREAK
	FLOODPLAIN

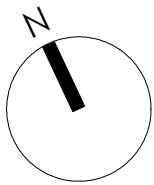

MONKS MOUNTAIN DRIVE

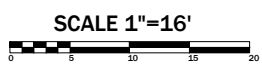

SHEET: 1 OF 1	PAPER: 8.5x11" SCALE: 1" = 16'	JOB NO. BY: JDB	DATE: 02.14.25	PROJECTS: 16200 MONDKS MOUNTAIN DRIVE 0.195 ACRES OUT OF THE B.K. STEWART SURVEY NO. 84, ABS. 2453	SHEET DESCRIPTION: OSSF PRELIMINARY DESIGN	BETTRIDGE SYSTEMS, LLC JIM BETTRIDGE, R.S. 128 HIGHLANDER ST AUSTIN, TX 78734 512-814-7020