


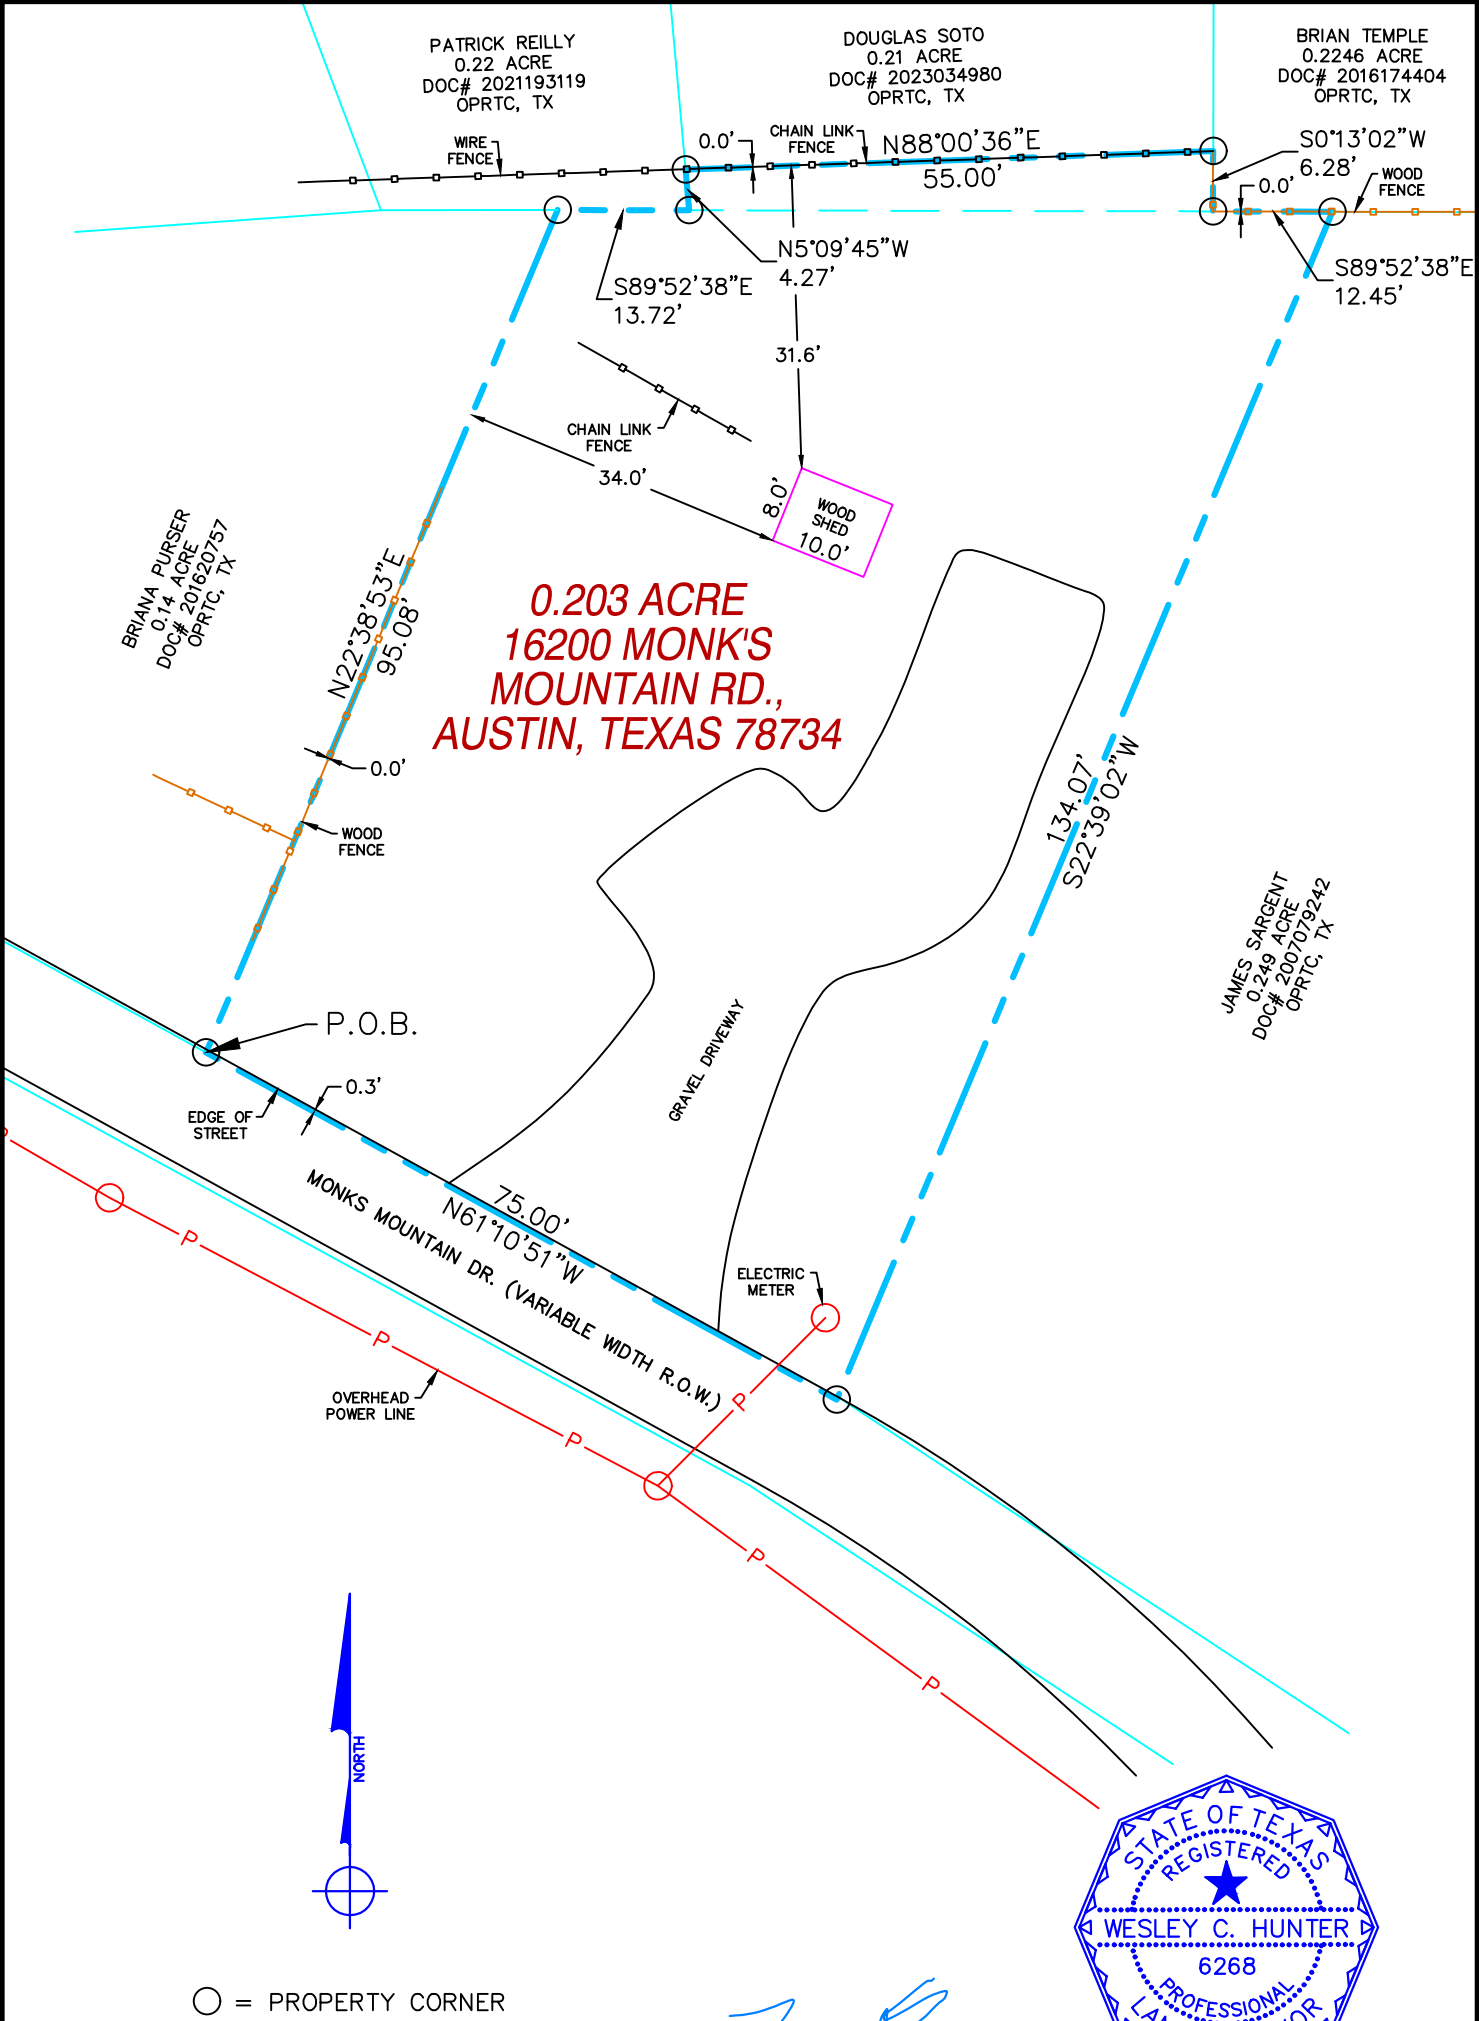

NOTES:

- ALL BEARINGS SHOWN HEREON ARE REFERENCED TO THE TEXAS PLANE COORDINATE SYSTEM, NORTH AMERICAN DATUM OF 1983, CENTRAL ZONE.
- THE SURVEY WAS PERFORMED WITH THE BENEFIT OF A TITLE COMMITMENT G. F. NO. 2501943-ROL ISSUED BY TITLE RESOURCES GUARANTY COMPANY, ISSUED JANUARY 23, 2025, EFFECTIVE JANUARY 13, 2025.
- PROPERTY IS SUBJECT TO THE RESTRICTIONS RECORDED IN VOLUME 2671, PAGE 441, VOLUME 3195, PAGE 310, VOLUME 4355, PAGE 1352, DEED RECORDS, VOLUME 9943, PAGE 255, REAL PROPERTY RECORDS, TRAVIS COUNTY, TEXAS.
- PROPERTY IS SUBJECT TO THE 20' WIDE POWER LINE EASEMENTS RECORDED IN VOLUME 413, PAGE 18 AND VOLUME 680, PAGE 35, DEED RECORDS, TRAVIS COUNTY, TEXAS.
- PROPERTY IS NOT SUBJECT TO THE EASEMENTS RECORDED IN VOLUME 586, PAGE 321; VOLUME 608, PAGE 48; VOLUME 643, PAGE 24; VOLUME 824, PAGE 337; VOLUME 960, PAGE 294; AND VOLUME 1525, PAGE 249, DEED RECORDS, TRAVIS COUNTY, TEXAS.
- ACCORDING TO THE FEMA FLOOD INSURANCE RATE MAP FOR TRAVIS COUNTY, TEXAS, MAP NUMBER 48453C0215J, EFFECTIVE JANUARY 22, 2020, SHOWS THIS TRACT TO BE IN ZONE "X", AREAS DETERMINED TO BE OUTSIDE THE 0.2% ANNUAL CHANCE FLOODPLAIN.

WESLEY C. HUNTER
REGISTERED PROFESSIONAL LAND SURVEYOR
NO. 6268

I, Wesley C. Hunter, a Registered Professional Land Surveyor in the State of Texas, License Number 6268, do hereby certify this plat to represent a survey made on the ground in the Month of January, 2025 under my direction and supervision, and the corner monuments shown hereon were found in compliance with the minimum requirements of a Category 1A, Condition II Land Title Survey and in accordance with the rules and regulations of the State of Texas.

BEING A 0.203 ACRE TRACT OF LAND LYING IN THE B. K. STEWART SURVEY NO. 84, ABSTRACT NO. 2453, TRAVIS COUNTY, TEXAS, AND BEING COMPRISED OF A 0.195 ACRE TRACT OF LAND DESCRIBED IN DOCUMENT NO. 2008001581, AND CONVEYED IN DOCUMENT NO. 200985343, OFFICIAL PUBLIC RECORDS, TRAVIS COUNTY, TEXAS, AND A A PORTION OF AN ALLEYWAY CONVEYED IN DOCUMENT NO. 201015506, OFFICIAL PUBLIC RECORDS, TRAVIS COUNTY, TEXAS.

DRAWN BY: WH	DATE: 1/30/2025	DWG. NO.	REV.
CHECKED BY: WH	DATE: 1/30/2025	HS-BKS84-0.203AC-001	0
SCALE: 1"=20'	APP.: 1/30/2025	GF#: 2501943-ROL	

HUNTER SURVEYING
819 CAMEL BACK DR., NEW BRAUNFELS, TX 78130
(830) 624-9192 TEXASSURVEYOR1@GMAIL.COM
FIRM # 10194098 REGULATED BY THE TEXAS BOARD OF PROFESSIONAL LAND SURVEYING